
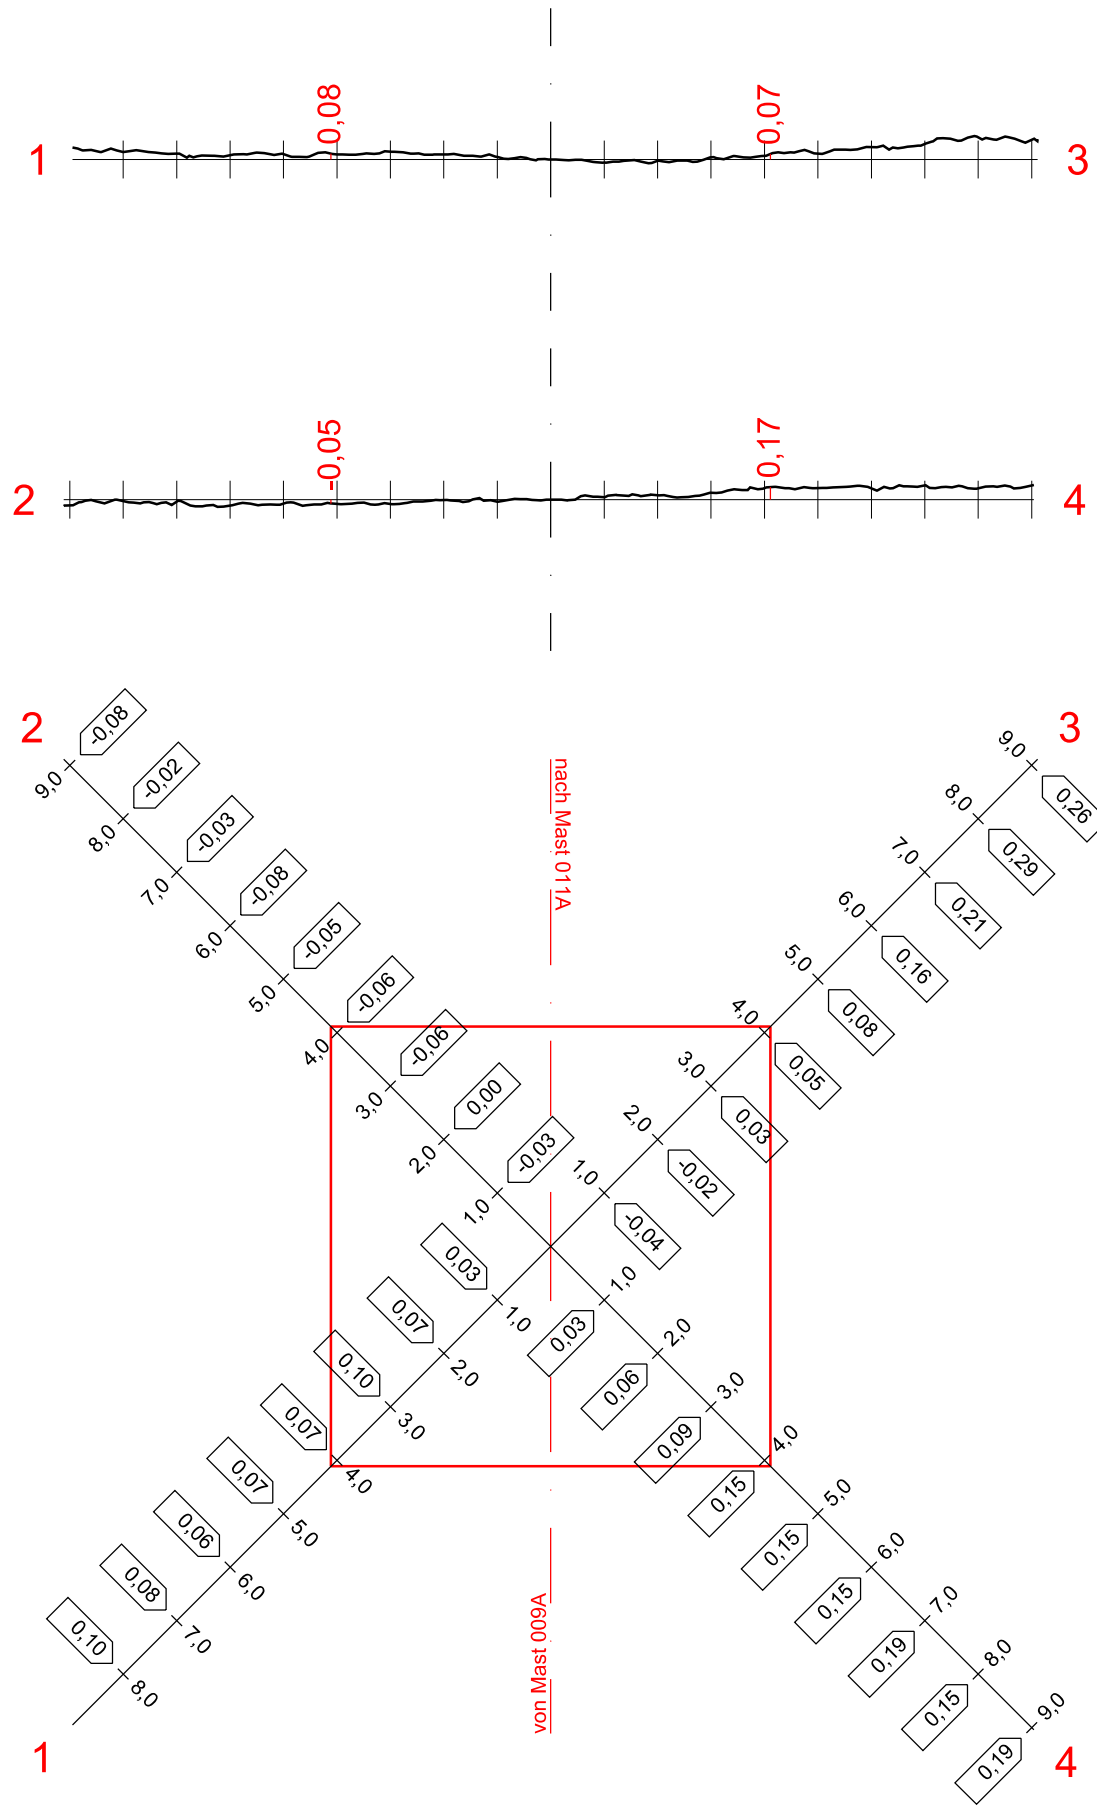


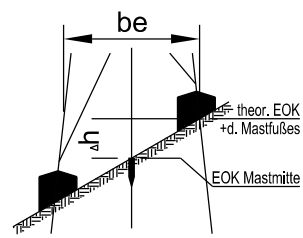

Mast-Nr. 010A	Gestänge:	D48-2002-11	Typ:	TD S3 28,50		
	b _e [m] =	5,82		BZ [mm/m] = 80		
fortl. Länge Mastmitte [m]		570,2	Höhe EOK Mastmitte über NN [m]: 106,30			
theor. Höhe-EOK des 0-Mastfußes über Mastmitte Δh (m) =		0,17	Mastfuß			
			1	2	3	4
Höhe über EOK Mastmitte	[m]	±	0,08	-0,05	0,07	0,17
Höhe über EOK Δh 0-Mastfuß	[m]	±	-0,09	-0,22	-0,09	0,00
erforderliche Schrägfüße [m]			0,00	0,00	0,00	0,00
Diagonalmaß D/2 Mastfuß [m]			4,11	4,11	4,11	4,11

Fußstuhl: 					
	Lfd-Nr.	Datum	Name	Änderungen	
	Aufnahme	12.2014	Laser	Trassierungsfirma: eqos Energie EQOS Energie Deutschland GmbH Wolfentalstraße 29 D-88400 Biberach	
	Gezeichnet	24.02.2020	Gruse		
GK-Koordinate: R (Y): 3450302,82 m H (X): 5428613,50 m		Geprüft	03.03.2020	Emmenlauer	Leitungsnummer: Anlage7 X 0
Maßstab Profil 1:100 Lage 1:100		DIAGONALPROFIL 380-kV-Leitung Daxlanden-Eichstetten Mast-Nr. 010A			